



Balcon — les quatre vues

Le même balcon vu de face depuis l'intérieur, coupé au grand lobe et au petit lobe, et en plan. Les deux coupes montrent la même construction à ses deux profondeurs extrêmes : c'est là que se lit l'ondulation.


1 · ELEVATION INTERIEURE DU BALCON · 1:25

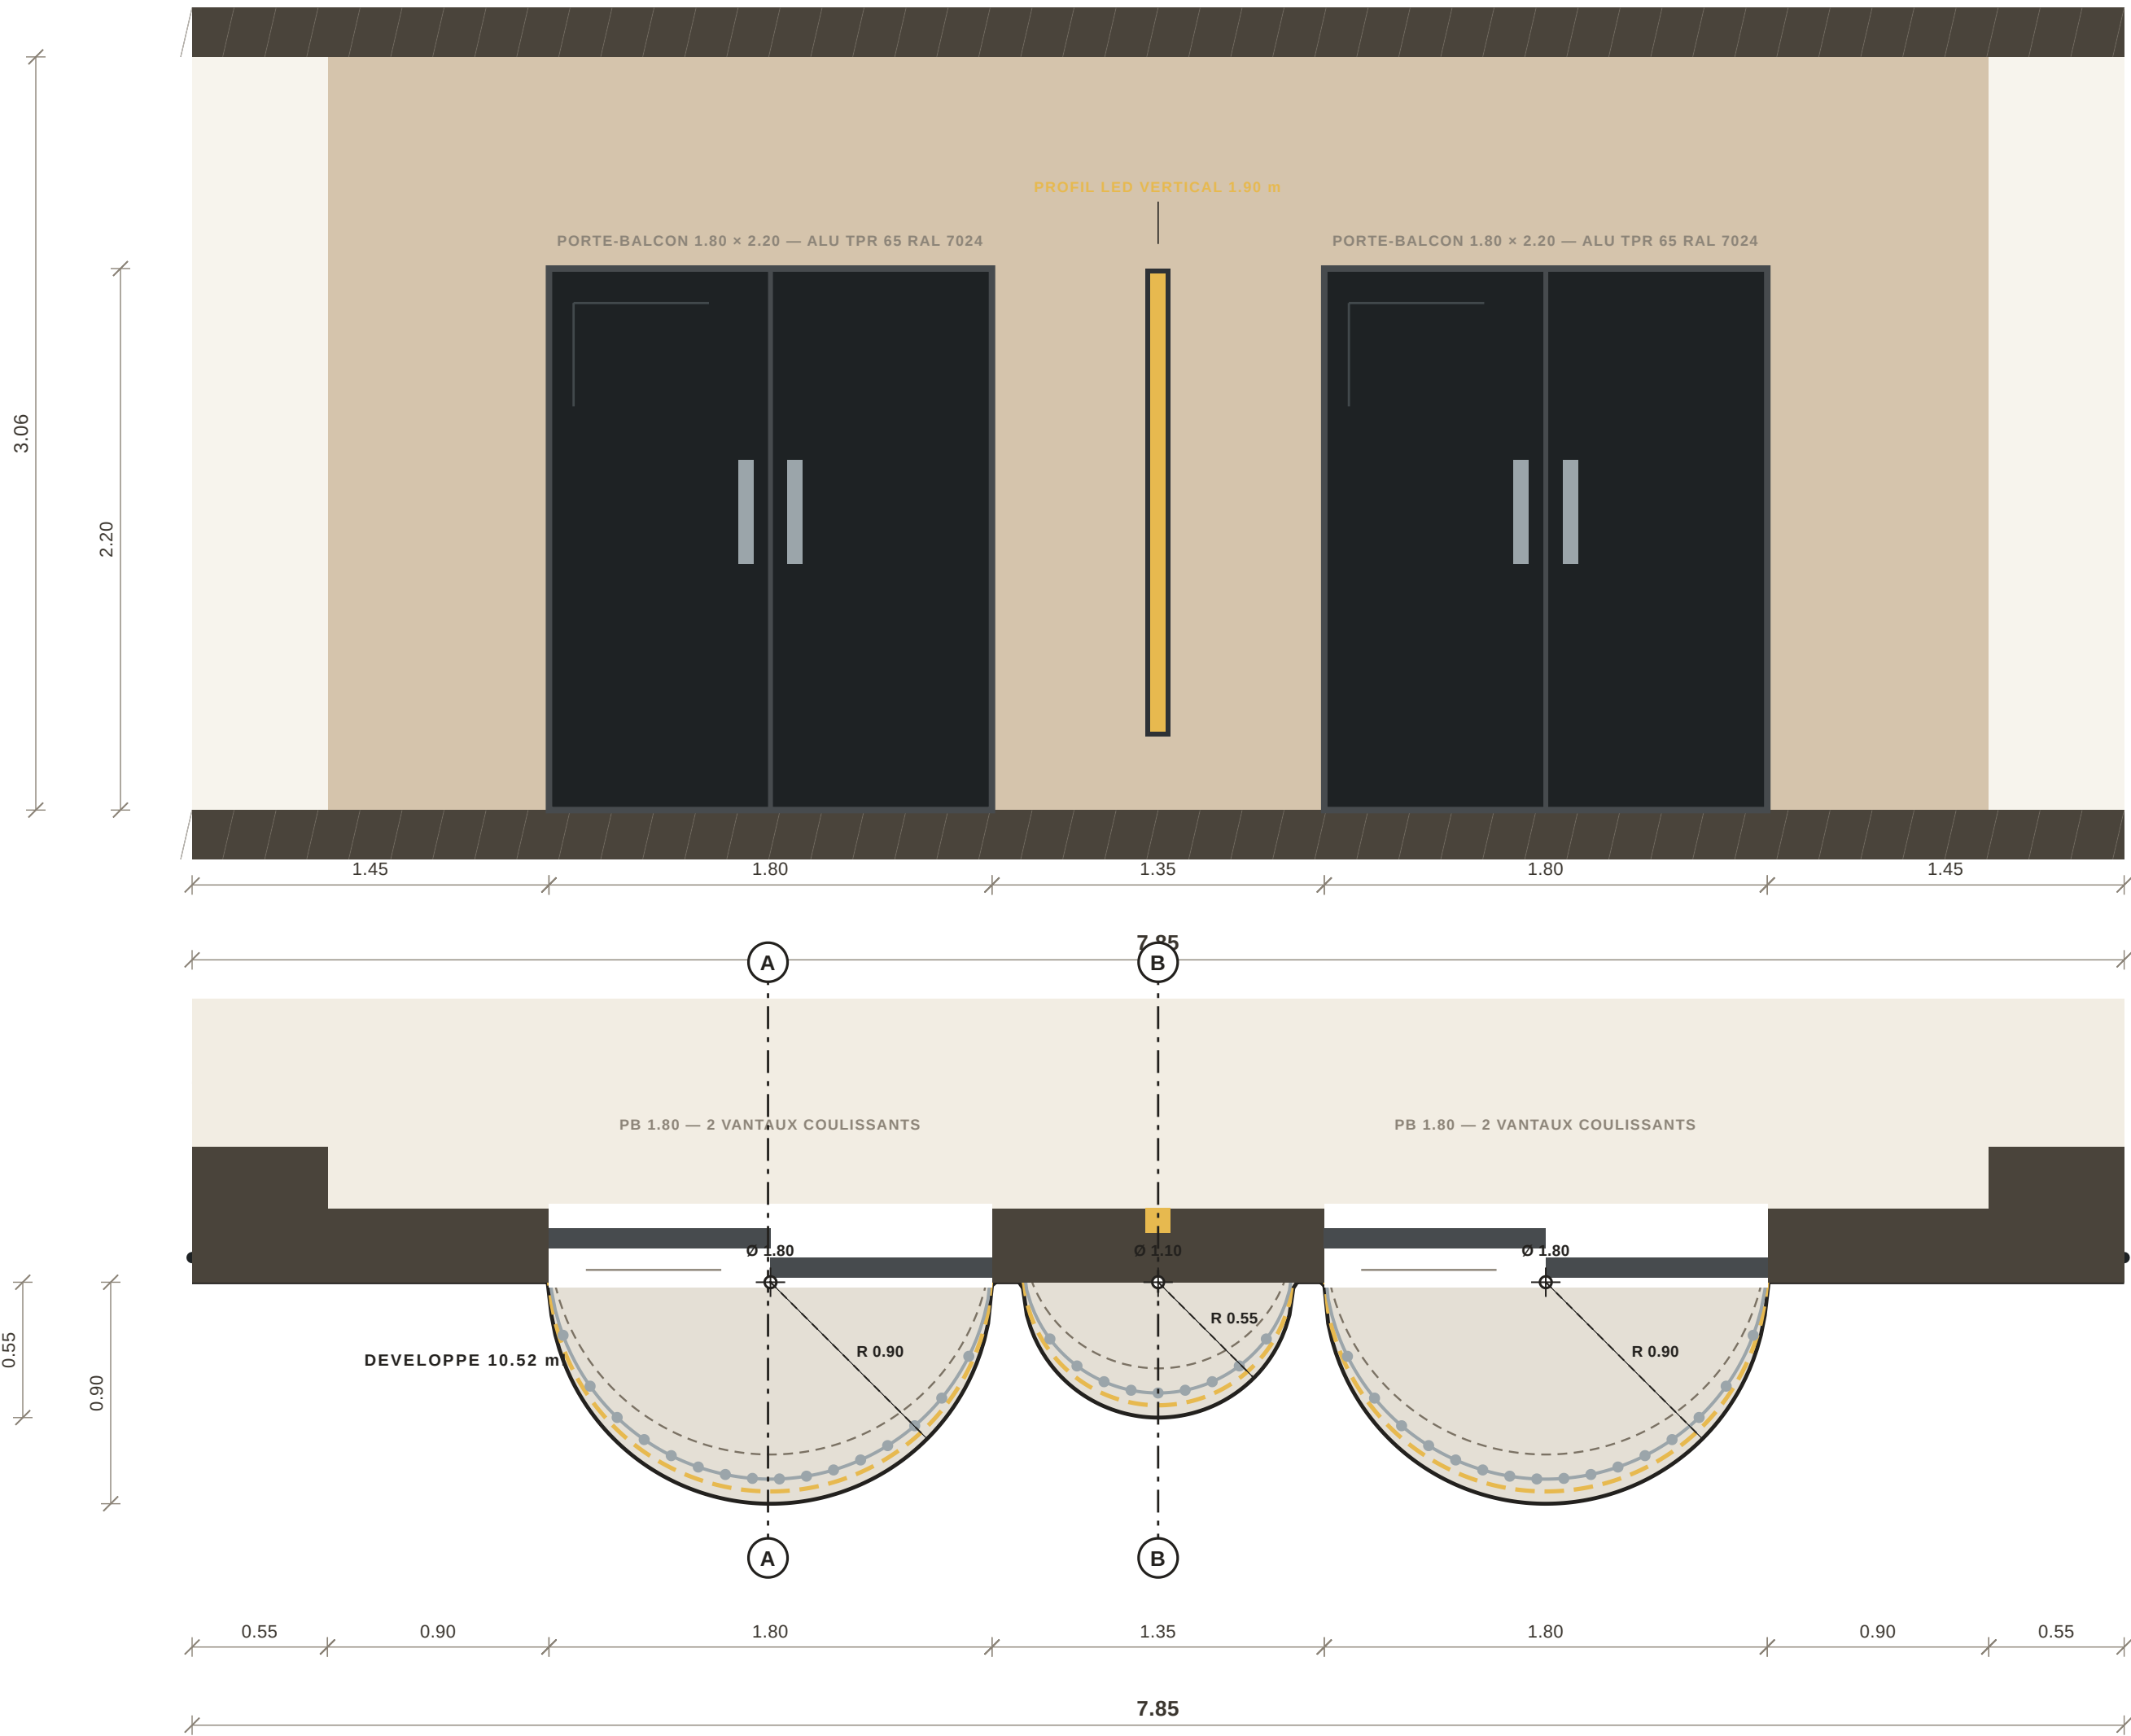

2 · COUPE A-A — AU GRAND LOBE (Ø 1.80) · 1:25

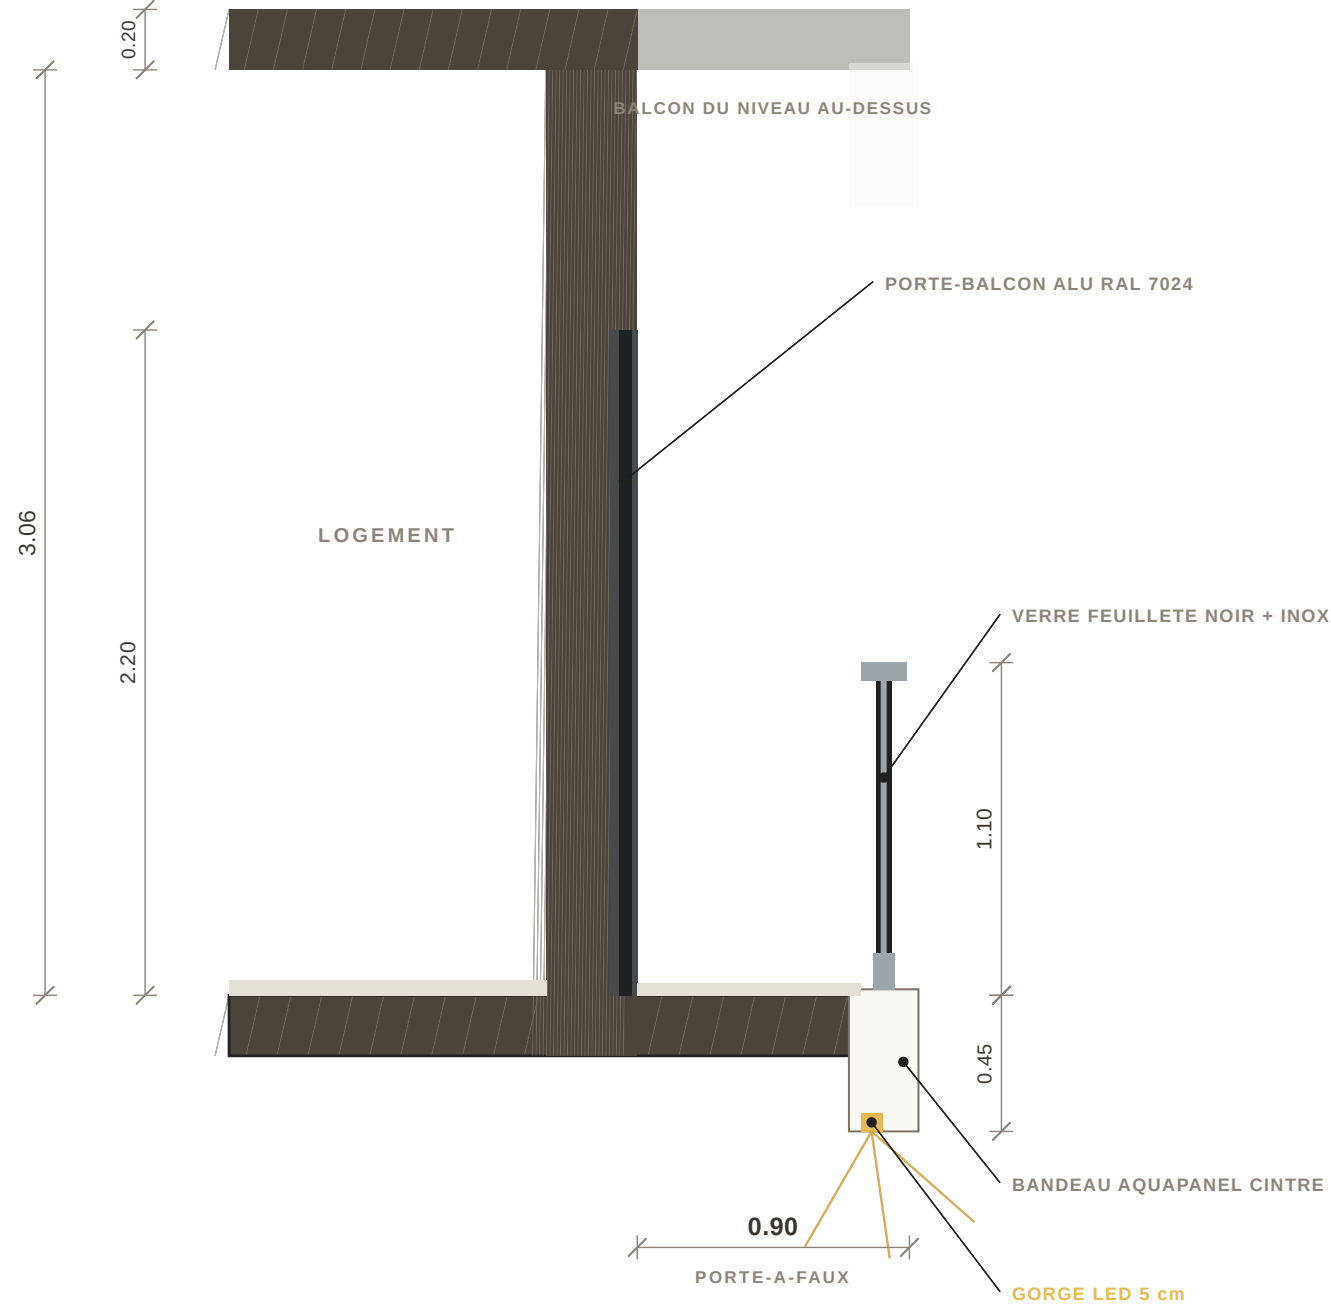

3 · COUPE B-B — AU PETIT LOBE (Ø 1.10) · 1:25

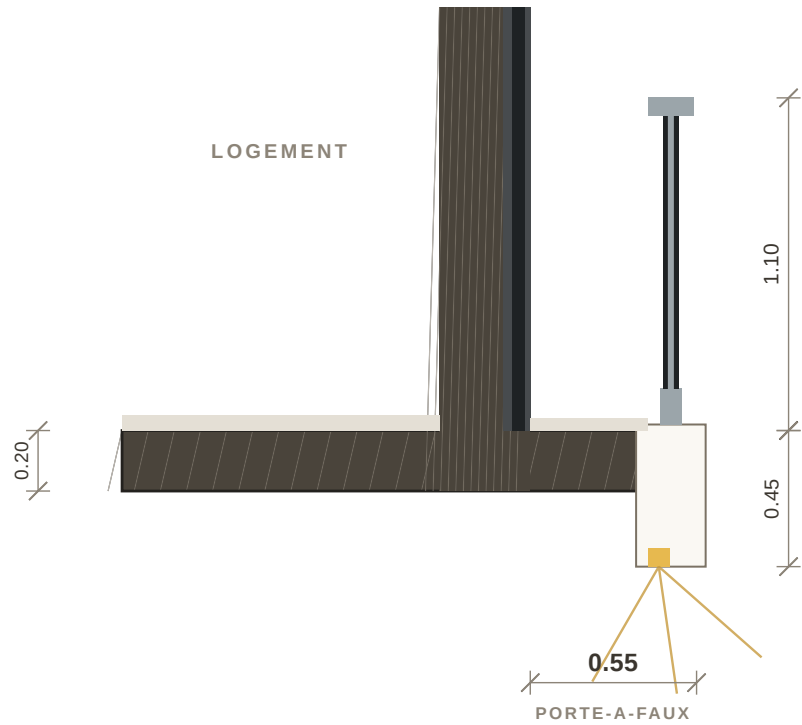

Bandeau de rive

Aquapanel cintré 12,5 mm sur ossature, retombée 0,45 m, finition blanche. Épaisseur d'habillage 0,20 m au nu de la dalle.

Gorge LED

Profil aluminium encastré de 5 cm en sous-face du bandeau, ruban LED 3000 K IP65 — alimentation à prévoir dans la dalle avant habillage.

Profil LED vertical

Garde-corps

Verre feuilleté teinté noir 8.8.4, montants et main courante inox Ø 42, h = 1,10 m au-dessus du sol fini. Barreaudage inox aux creux et aux crêtes.

Structure