


Avancée parking & terrasse

Le socle parking RDC + R+1 avance de 4.00 m sur le nu de façade ; sa toiture devient la terrasse du R+2. Au-dessus, les balcons en console suivent l'onde de rive, de 0 au nu de façade à 1,80 m au grand lobe — tracé arrêté sur votre croquis annoté. Hauteur libre 3,06 m, dalle 0,20 m ; RDC 2,60 m libre.

ÉCHELLE 1:100
COTES EN MÈTRES
ÉTAT PROJETÉ

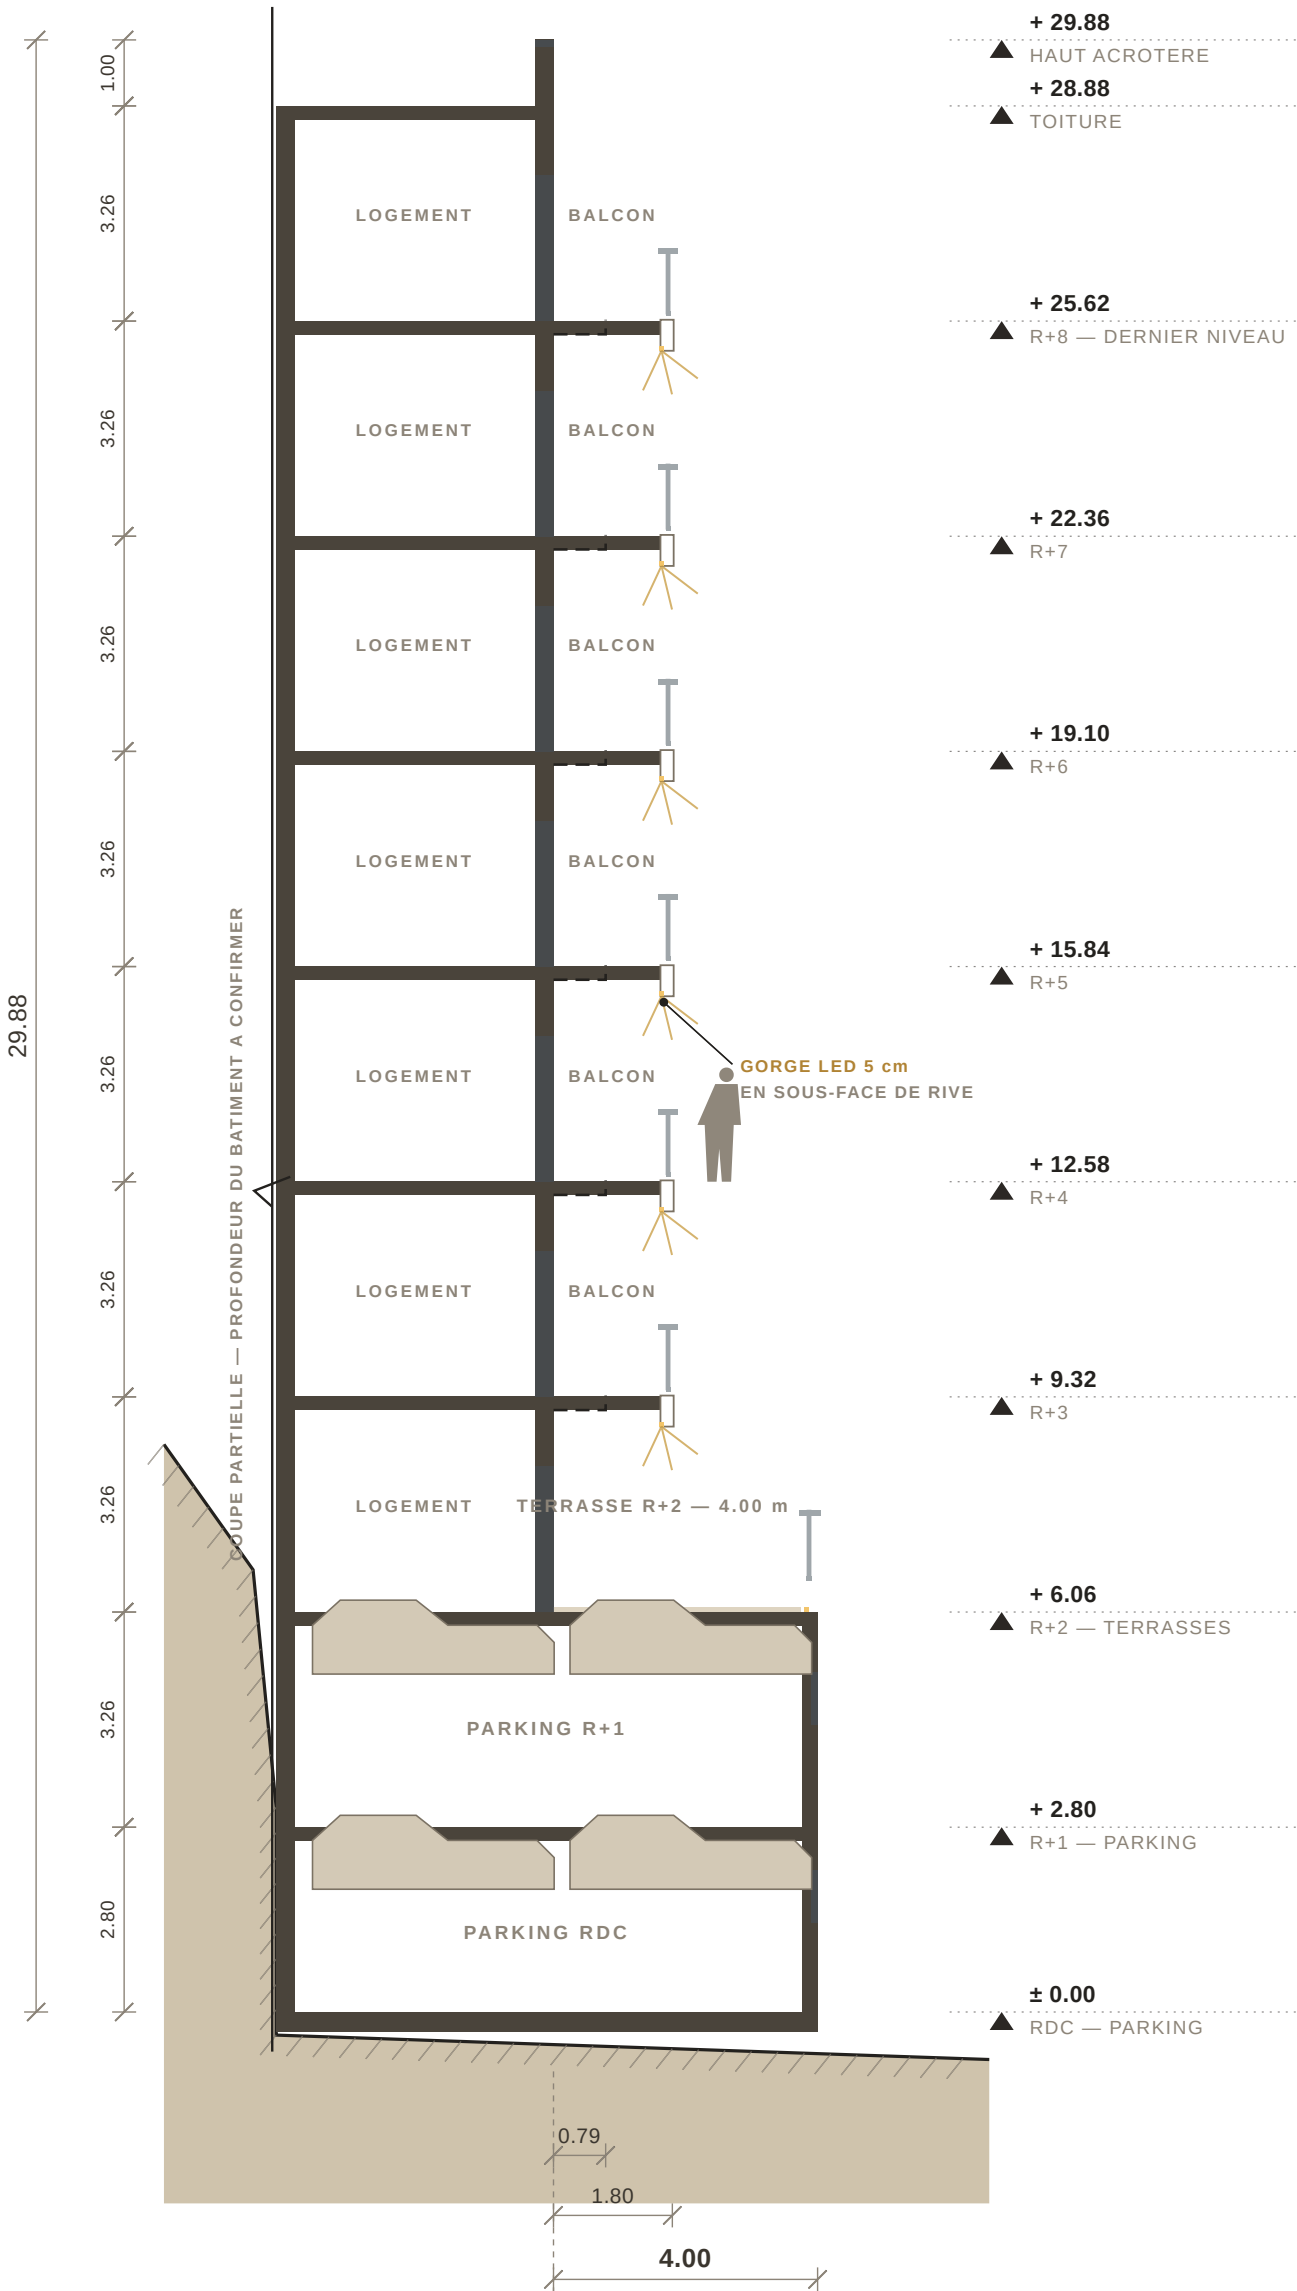

BALCON 0 AU NU → 1.80 m AU GRAND LOBE · AVANCEE DU PARKING 4.00 m SUR LE NU DE M

LES DEUX TERRASSES R+2 SONT SEPARÉES PAR LE VIDE CENTRAL — VOIR FACADE