



Balcon — les quatre vues

Le même balcon vu de face depuis l'intérieur, coupé au grand lobe (1,80 m) et au petit lobe (1,10 m), et en plan. Les deux coupes montrent la même construction à ses deux profondeurs extrêmes : c'est là que se lit l'ondulation.


1 · ELEVATION INTERIEURE DU BALCON · 1:25

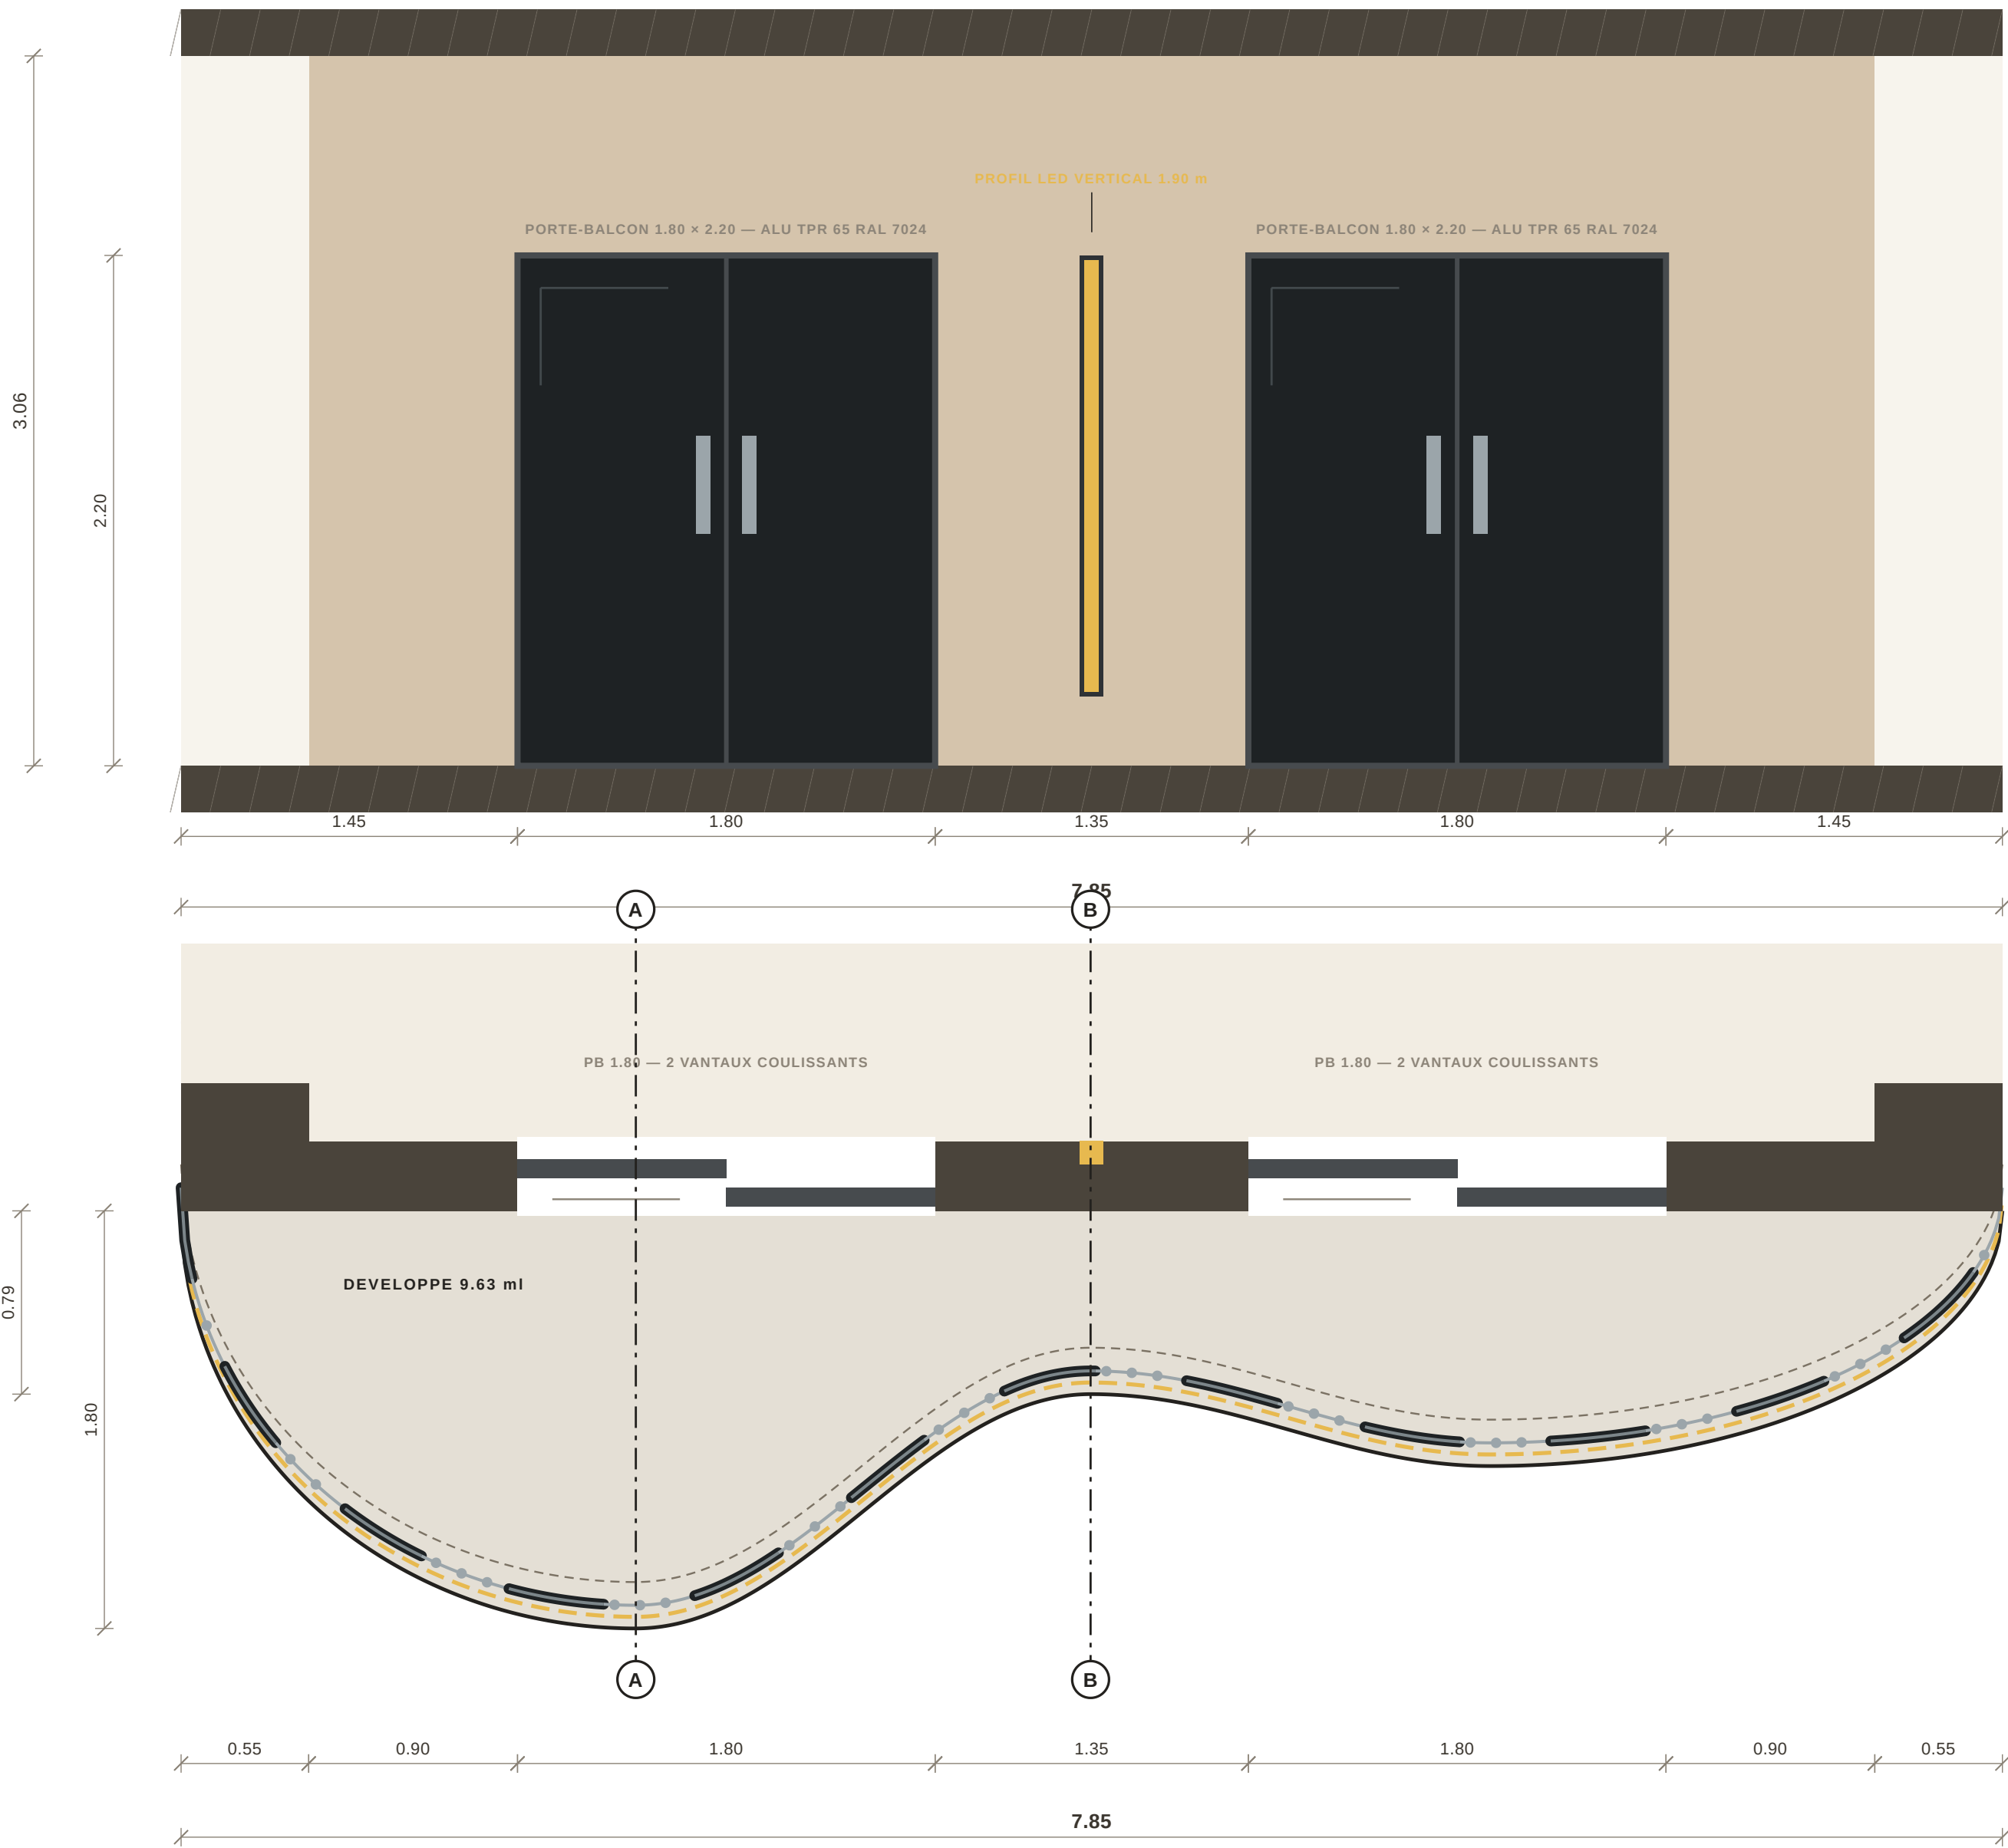

2 · COUPE A-A — AU GRAND LOBE · 1:25

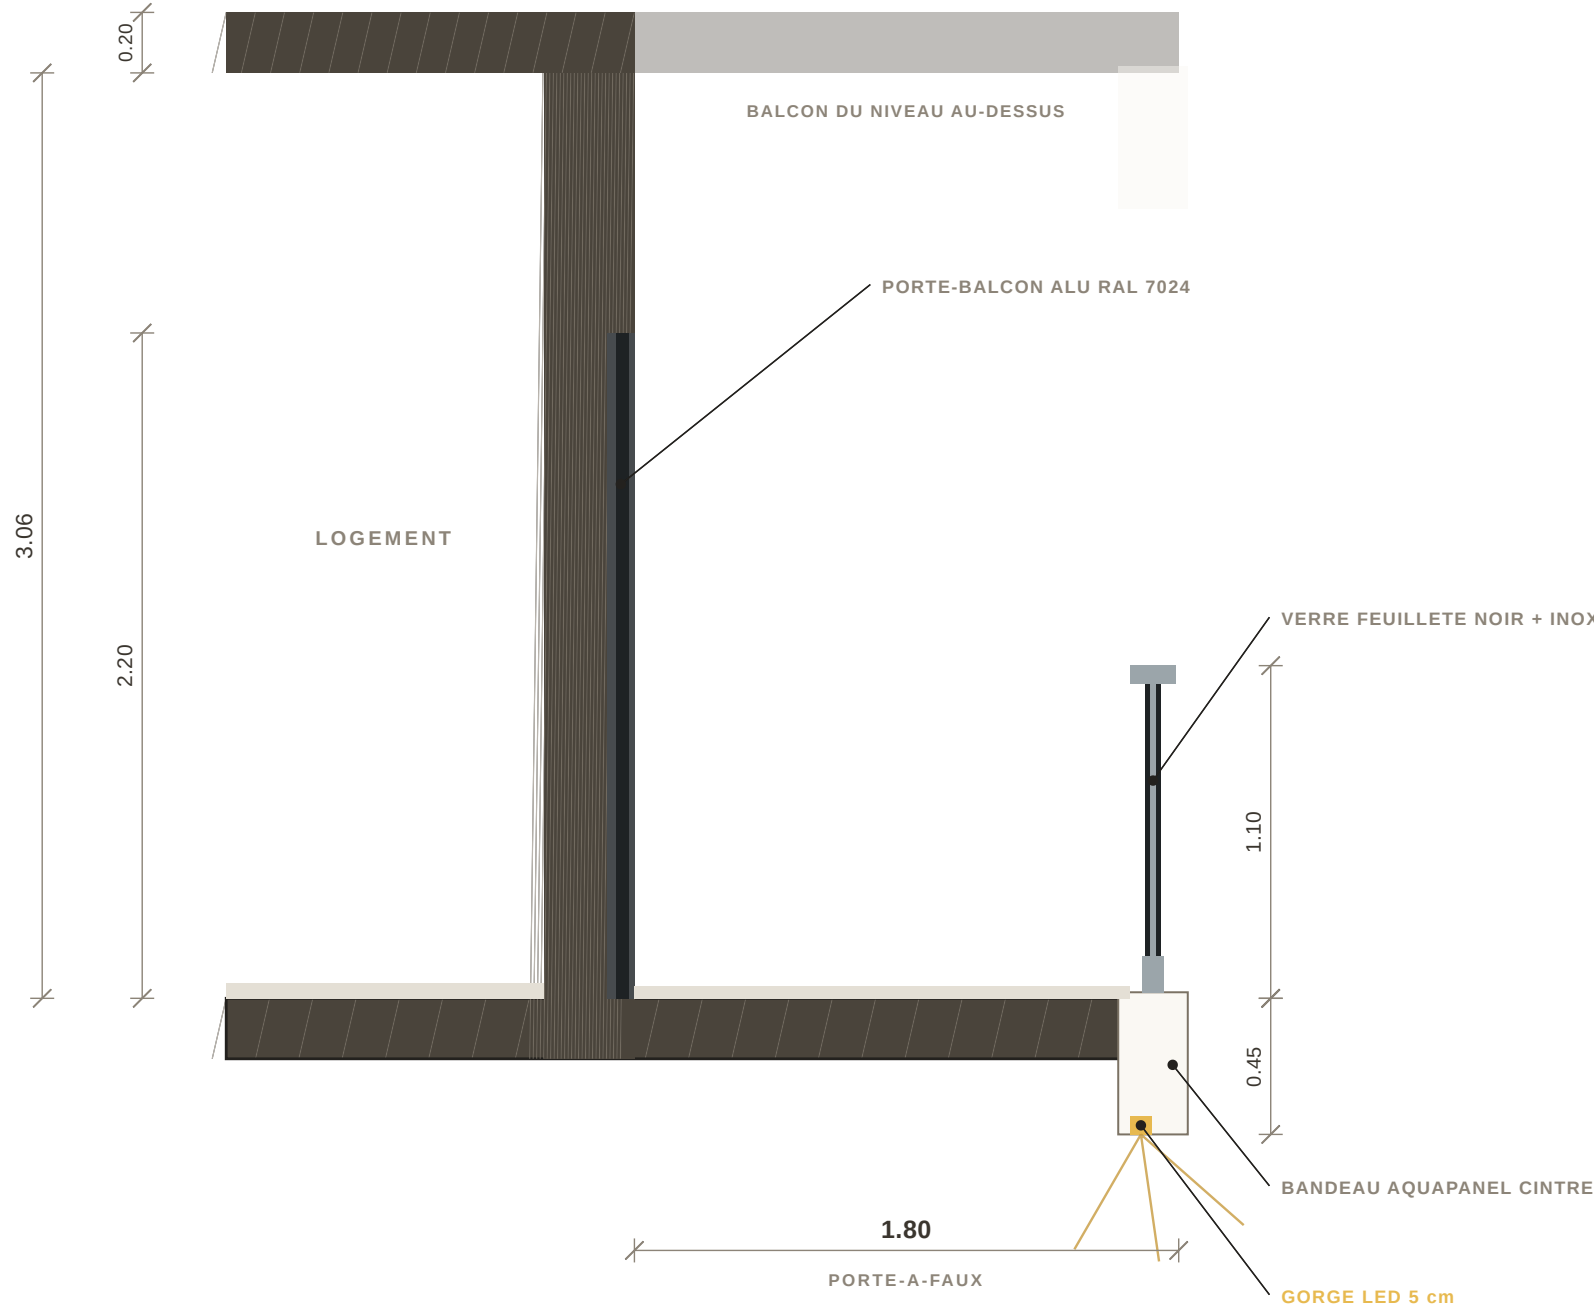

3 · COUPE B-B — AU PETIT LOBE · 1:25

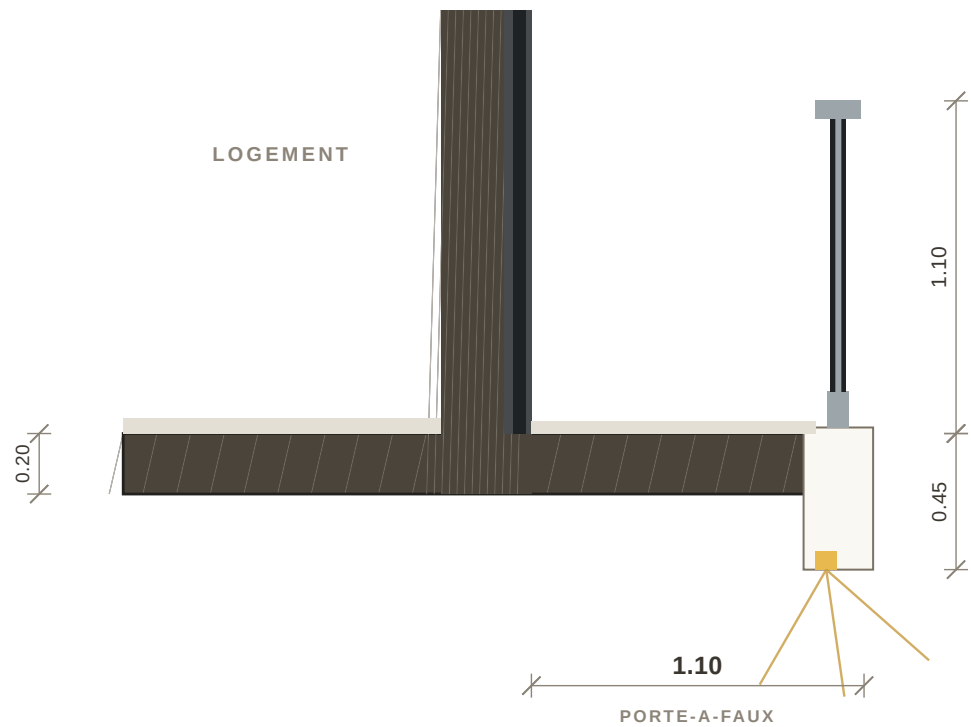

Bandeau de rive

Aquapanel cintré 12,5 mm sur ossature, retombée 0,45 m, finition blanche. Épaisseur d'habillage 0,20 m au nu de la dalle.

Porte-balcon

Aluminium TPR série 65 à rupture de pont thermique, RAL 7024, 2 vantaux coulissants, 1,80 × 2,20 m, double vitrage 4/16/4.

Gorge LED

Profil aluminium encastré de 5 cm en sous-face du bandeau, ruban LED 3000 K IP65 — alimentation à prévoir dans la dalle avant habillage.

Profil LED vertical

Encastré dans le trumeau entre les deux portes, 1,90 m de haut, même circuit que la gorge de rive.

Garde-corps

Alternance 40 cm / 40 cm sur tout le développé : un panneau de verre feuilleté 8.8.4 teinté noir, plat, puis 40 cm de barreaudage inox Ø 16. Main courante inox Ø 42, h = 1,10 m.

Structure

Dalle 0,20 m, hauteur libre 3,06 m. Console nulle au nu de façade, 1,80 m au grand lobe, 1,10 m au petit — ferrailage à valider par le BET.