


Comment la façade est faite, de bas en haut

Quatre coupes verticales au 1:10 : la rive du balcon avec son bandeau cintré et sa gorge LED, le seuil de la porte-balcon, la jonction du plancher avec le joint creux, et le couronnement. Cotes en mètres.

D1 · RIVE DE BALCON — AU GRAND LOBE

ÉCHELLE 1:10

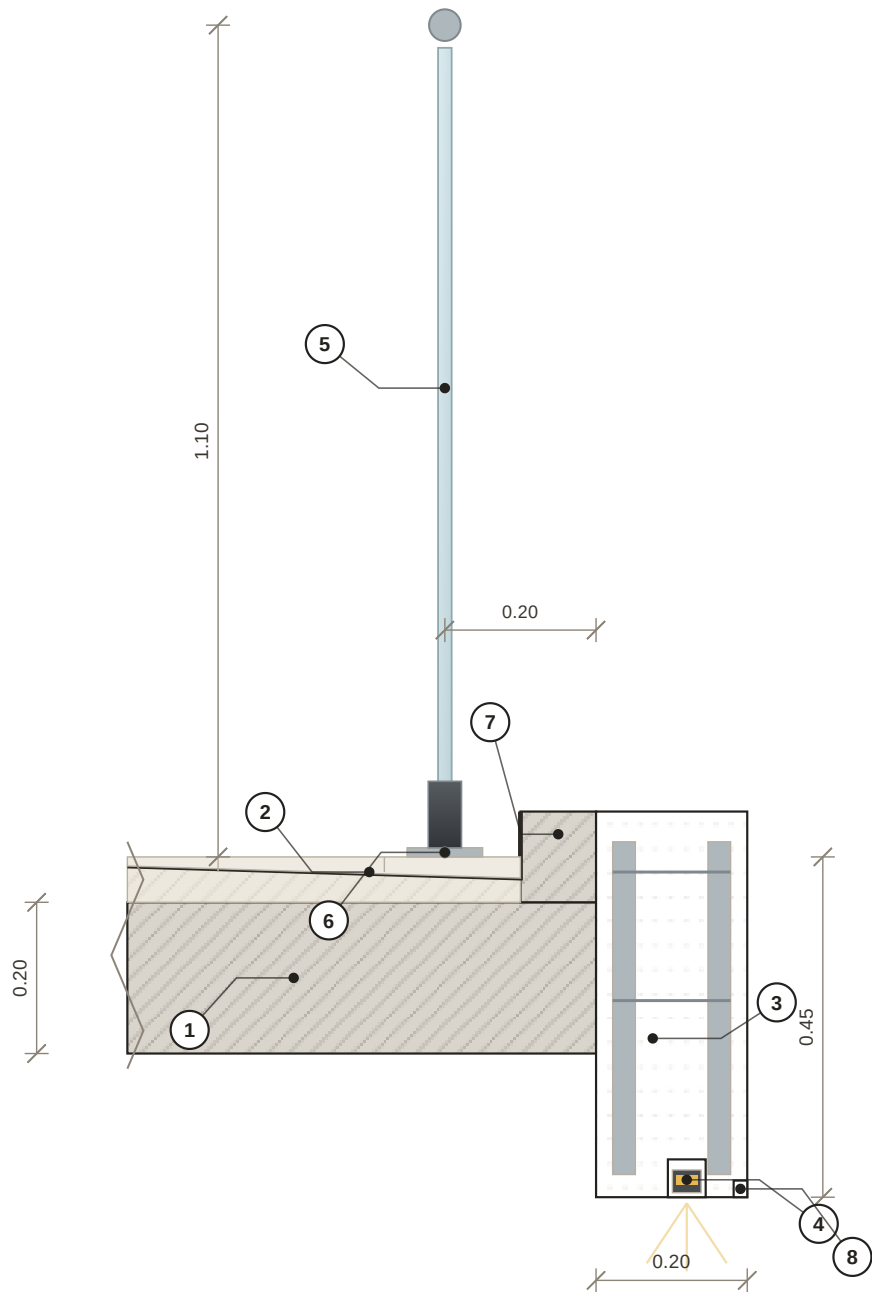


NOMENCLATURE

- ① Dalle BA 20 cm en porte-à-faux, coffrage cintré suivant l'onde
- ② Forme de pente 1,5 % + étanchéité SEL bicouche, relevé 12 cm
- ③ Ossature acier galvanisé cintrée + Aquapanel Outdoor 12,5 mm, enduit armé, monocouche blanc — habillage 20 cm au nu de la dalle
- ④ Gorge 50 × 50 mm, profil alu + ruban LED 3000 K IP65
- ⑤ Garde-corps h 1,10 m : 40 cm de verre feuilleté 8.8.4, 40 cm de barreaudage inox Ø 16, en alternance ; main courante inox Ø 42
- ⑥ Platine inox 100 × 100 × 8, 2 goudjons M10 inox, manchette d'étanchéité
- ⑦ Costière béton 10 × 12 cm en rive, support du relevé
- ⑧ Larmier 18 mm en pied de bandeau

D2 · SEUIL DE PORTE-BALCON

ÉCHELLE 1:10

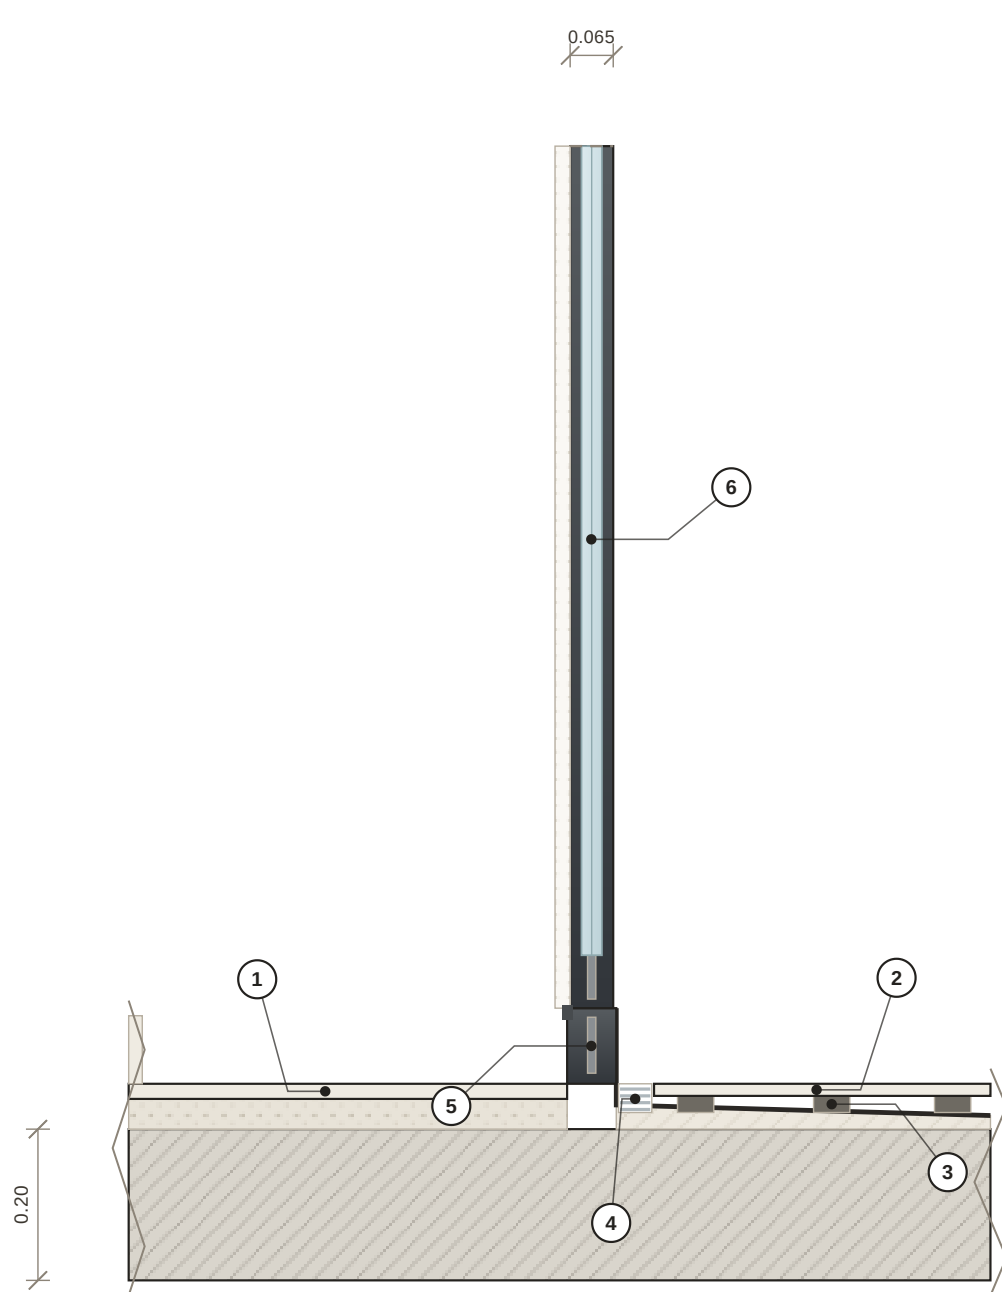


NOMENCLATURE

- ① Intérieur : carrelage sur chape, niveau fini de l'étage
- ② Balcon : grès cérame 60 × 60 sur plots réglables, 2 cm plus bas que l'intérieur — la pluie ne remonte jamais dans le logement
- ③ Plots PVC réglables, lame d'air ventilée sous le carrelage
- ④ Caniveau de rive 45 mm, grille inox, raccordé à la descente EP
- ⑤ Seuil aluminium à rupture de pont thermique, rejingot 10 cm, relevé d'étanchéité 12 cm derrière le dormant
- ⑥ Alu TPR série 65 RAL 7024, 2 vantaux coulissants, 4/16/4

D3 · JONCTION PLANCHER · LINTEAU · ALLÈGE

ÉCHELLE 1:10

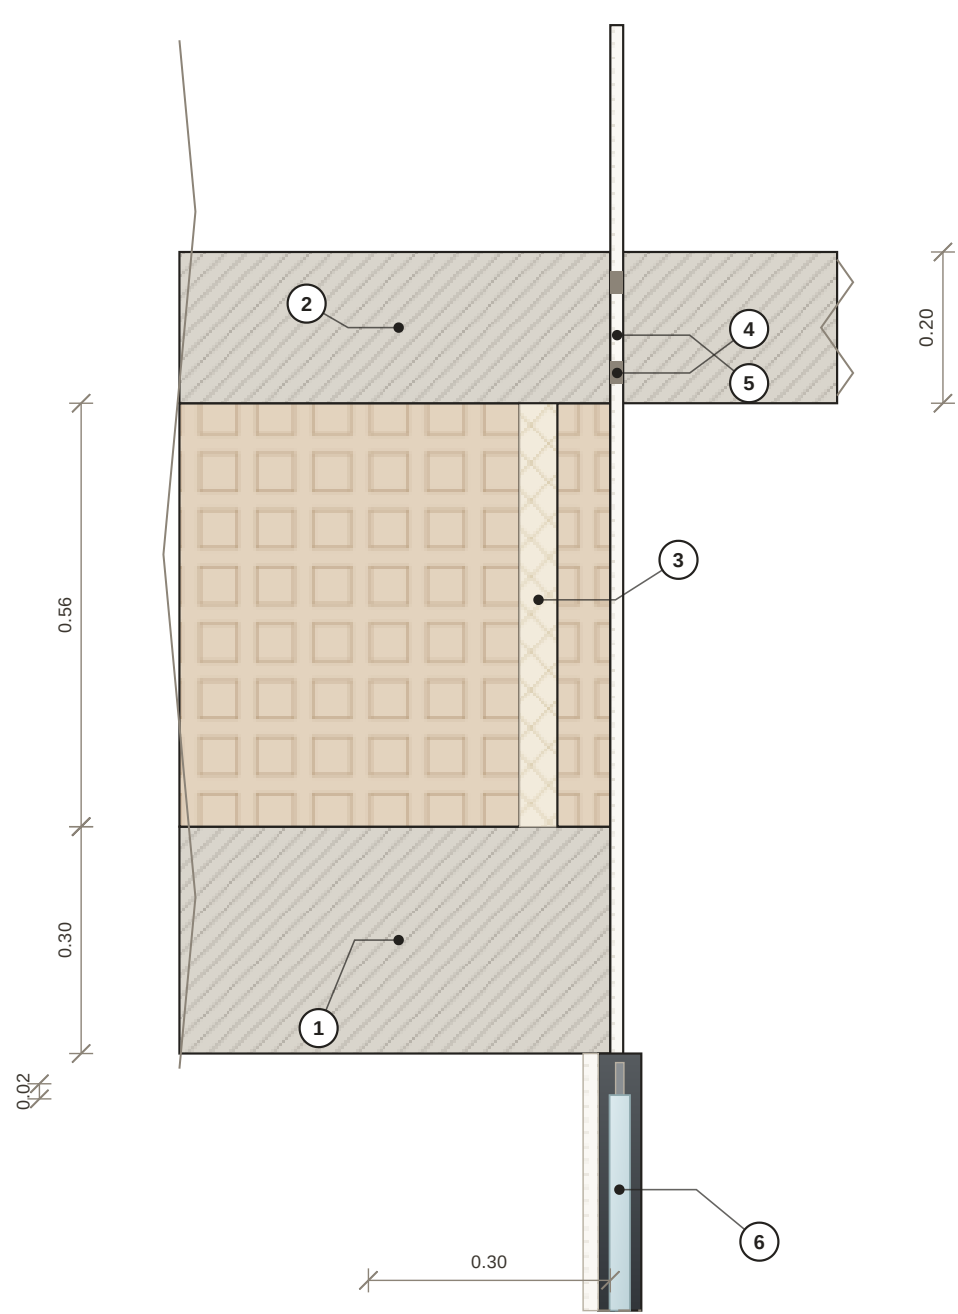


NOMENCLATURE

- ① Linteau BA 20 × 30 au-dessus de la porte-balcon
- ② Plancher dalle pleine BA 20 cm — hauteur sous plafond 3,06 m, hauteur d'étage 3,26 m
- ③ Double cloison brique creuse 15 + lame d'air 5 + brique 10
- ④ Joint creux 15 × 15 mm au droit de chaque plancher : il rattrape le retrait du monocouche et dessine la ligne d'étage
- ⑤ Monocouche blanc 15 mm, grain fin gratté, sur gobetis
- ⑥ Dormant haut alu TPR 65, calfeutrement mousse + mastic

D4 · ACROTÈRE ET COUVERTINE

ÉCHELLE 1:10

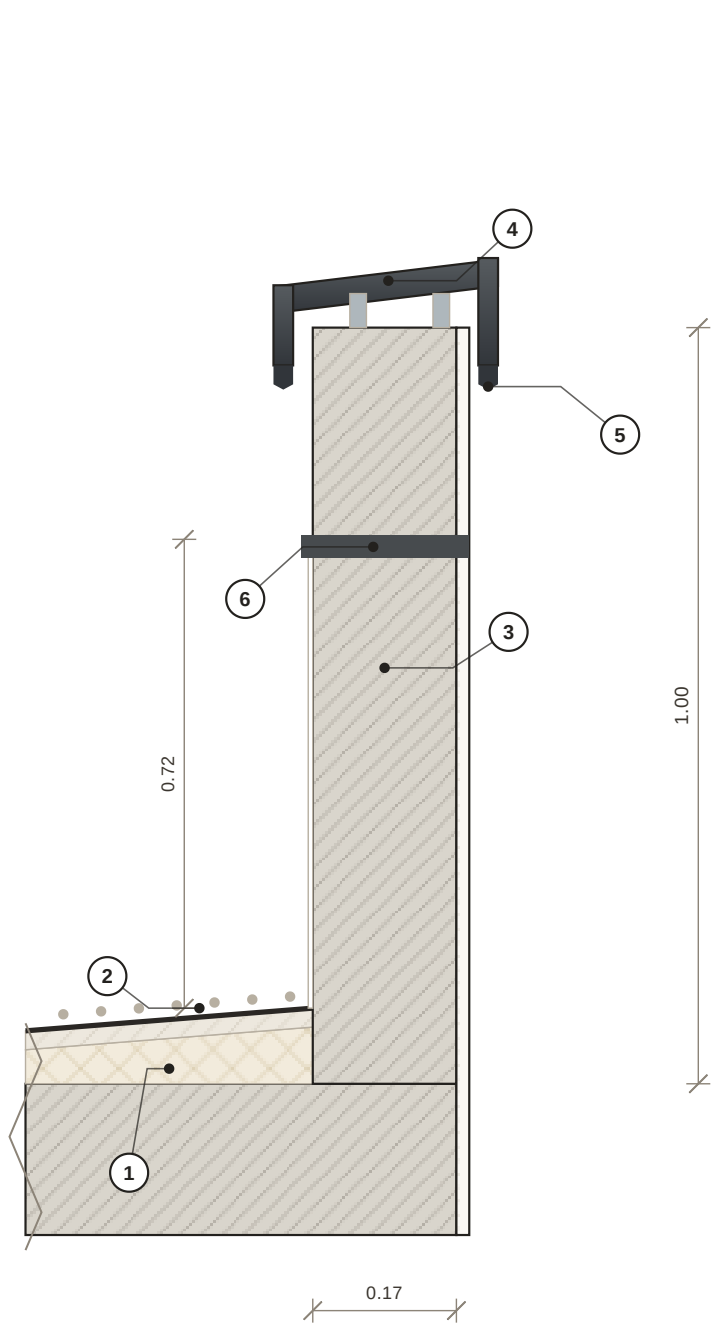

NOMENCLATURE

- ① Toiture inaccessible : dalle BA 20, isolant en pente 1,5 %
- ② Étanchéité bicouche + protection gravillons roulés 4 cm
- ③ Acrotère BA 17 cm, hauteur 1,00 m au-dessus du niveau fini
- ④ Couvitrine aluminium RAL 7024, pente vers l'intérieur, éclisses et pattes de fixation tous les 1,20 m
- ⑤ Goutte d'eau des deux côtés — elle décolle l'eau du monocouche : c'est elle qui empêche les coulures noires sous le couronnement
- ⑥ Relevé d'étanchéité 30 cm + bande solin en tête