


La façade coupée à hauteur d’homme

Trois coupes horizontales au 1:10, plan de coupe à +1,50 m du sol fini : le poteau de 55 cm avec le tableau de la baie, le trumeau de 1,35 m qui porte le profil LED vertical, et le vide central avec ses deux balcons séparés par le brise-vue de 40 cm.

H1 · POTEAU 55 cm ET TABLEAU DE BAIE

ÉCHELLE 1:10 · COUPE HORIZONTALE À +1,50

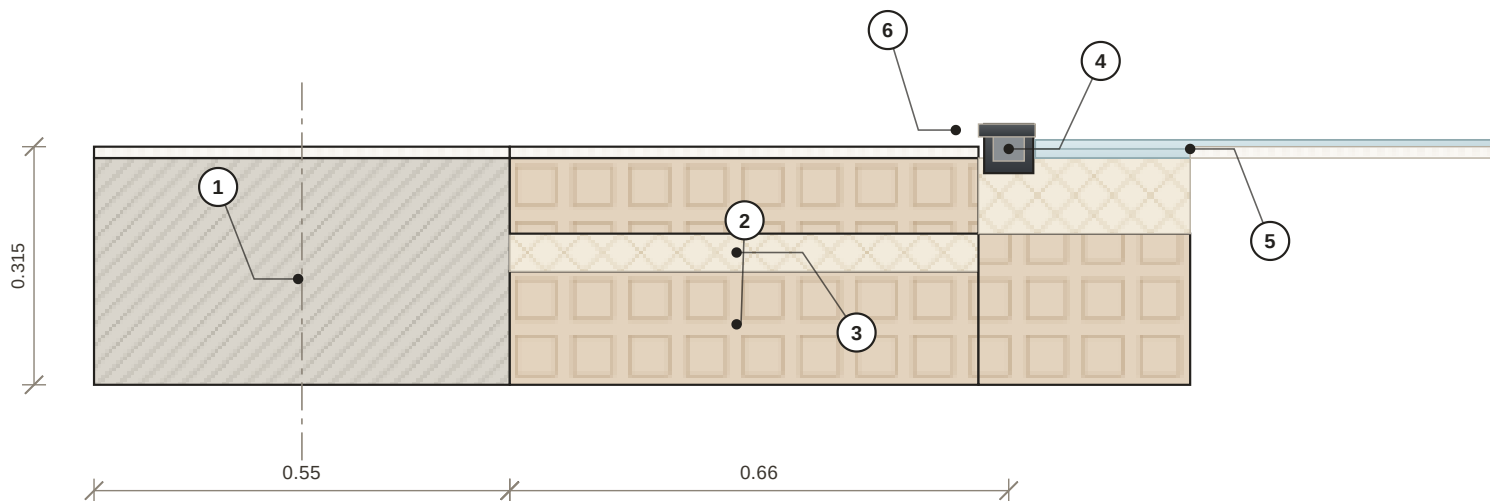


NOMENCLATURE

- ① Poteau BA 55 × 30 — c'est lui qui donne la trame de la façade
- ② Double cloison brique creuse 15 + lame d'air 5 + brique 10
- ③ Retour de tableau : la brique intérieure vient buter sur le dormant, la lame d'air est fermée par un about isolant
- ④ Dormant latéral alu TPR 65 à rupture de pont thermique, RAL 7024
- ⑤ Double vitrage 4/16/4, joint EPDM, calage périphérique
- ⑥ Couvre-joint alu et mastic sur fond de joint, 8 mm

H3 · LE VIDE CENTRAL — DEUX BALCONS, LE BRISE-VUE ENTRE EUX

ÉCHELLE 1:10 · COUPE HORIZONTALE À +1,50

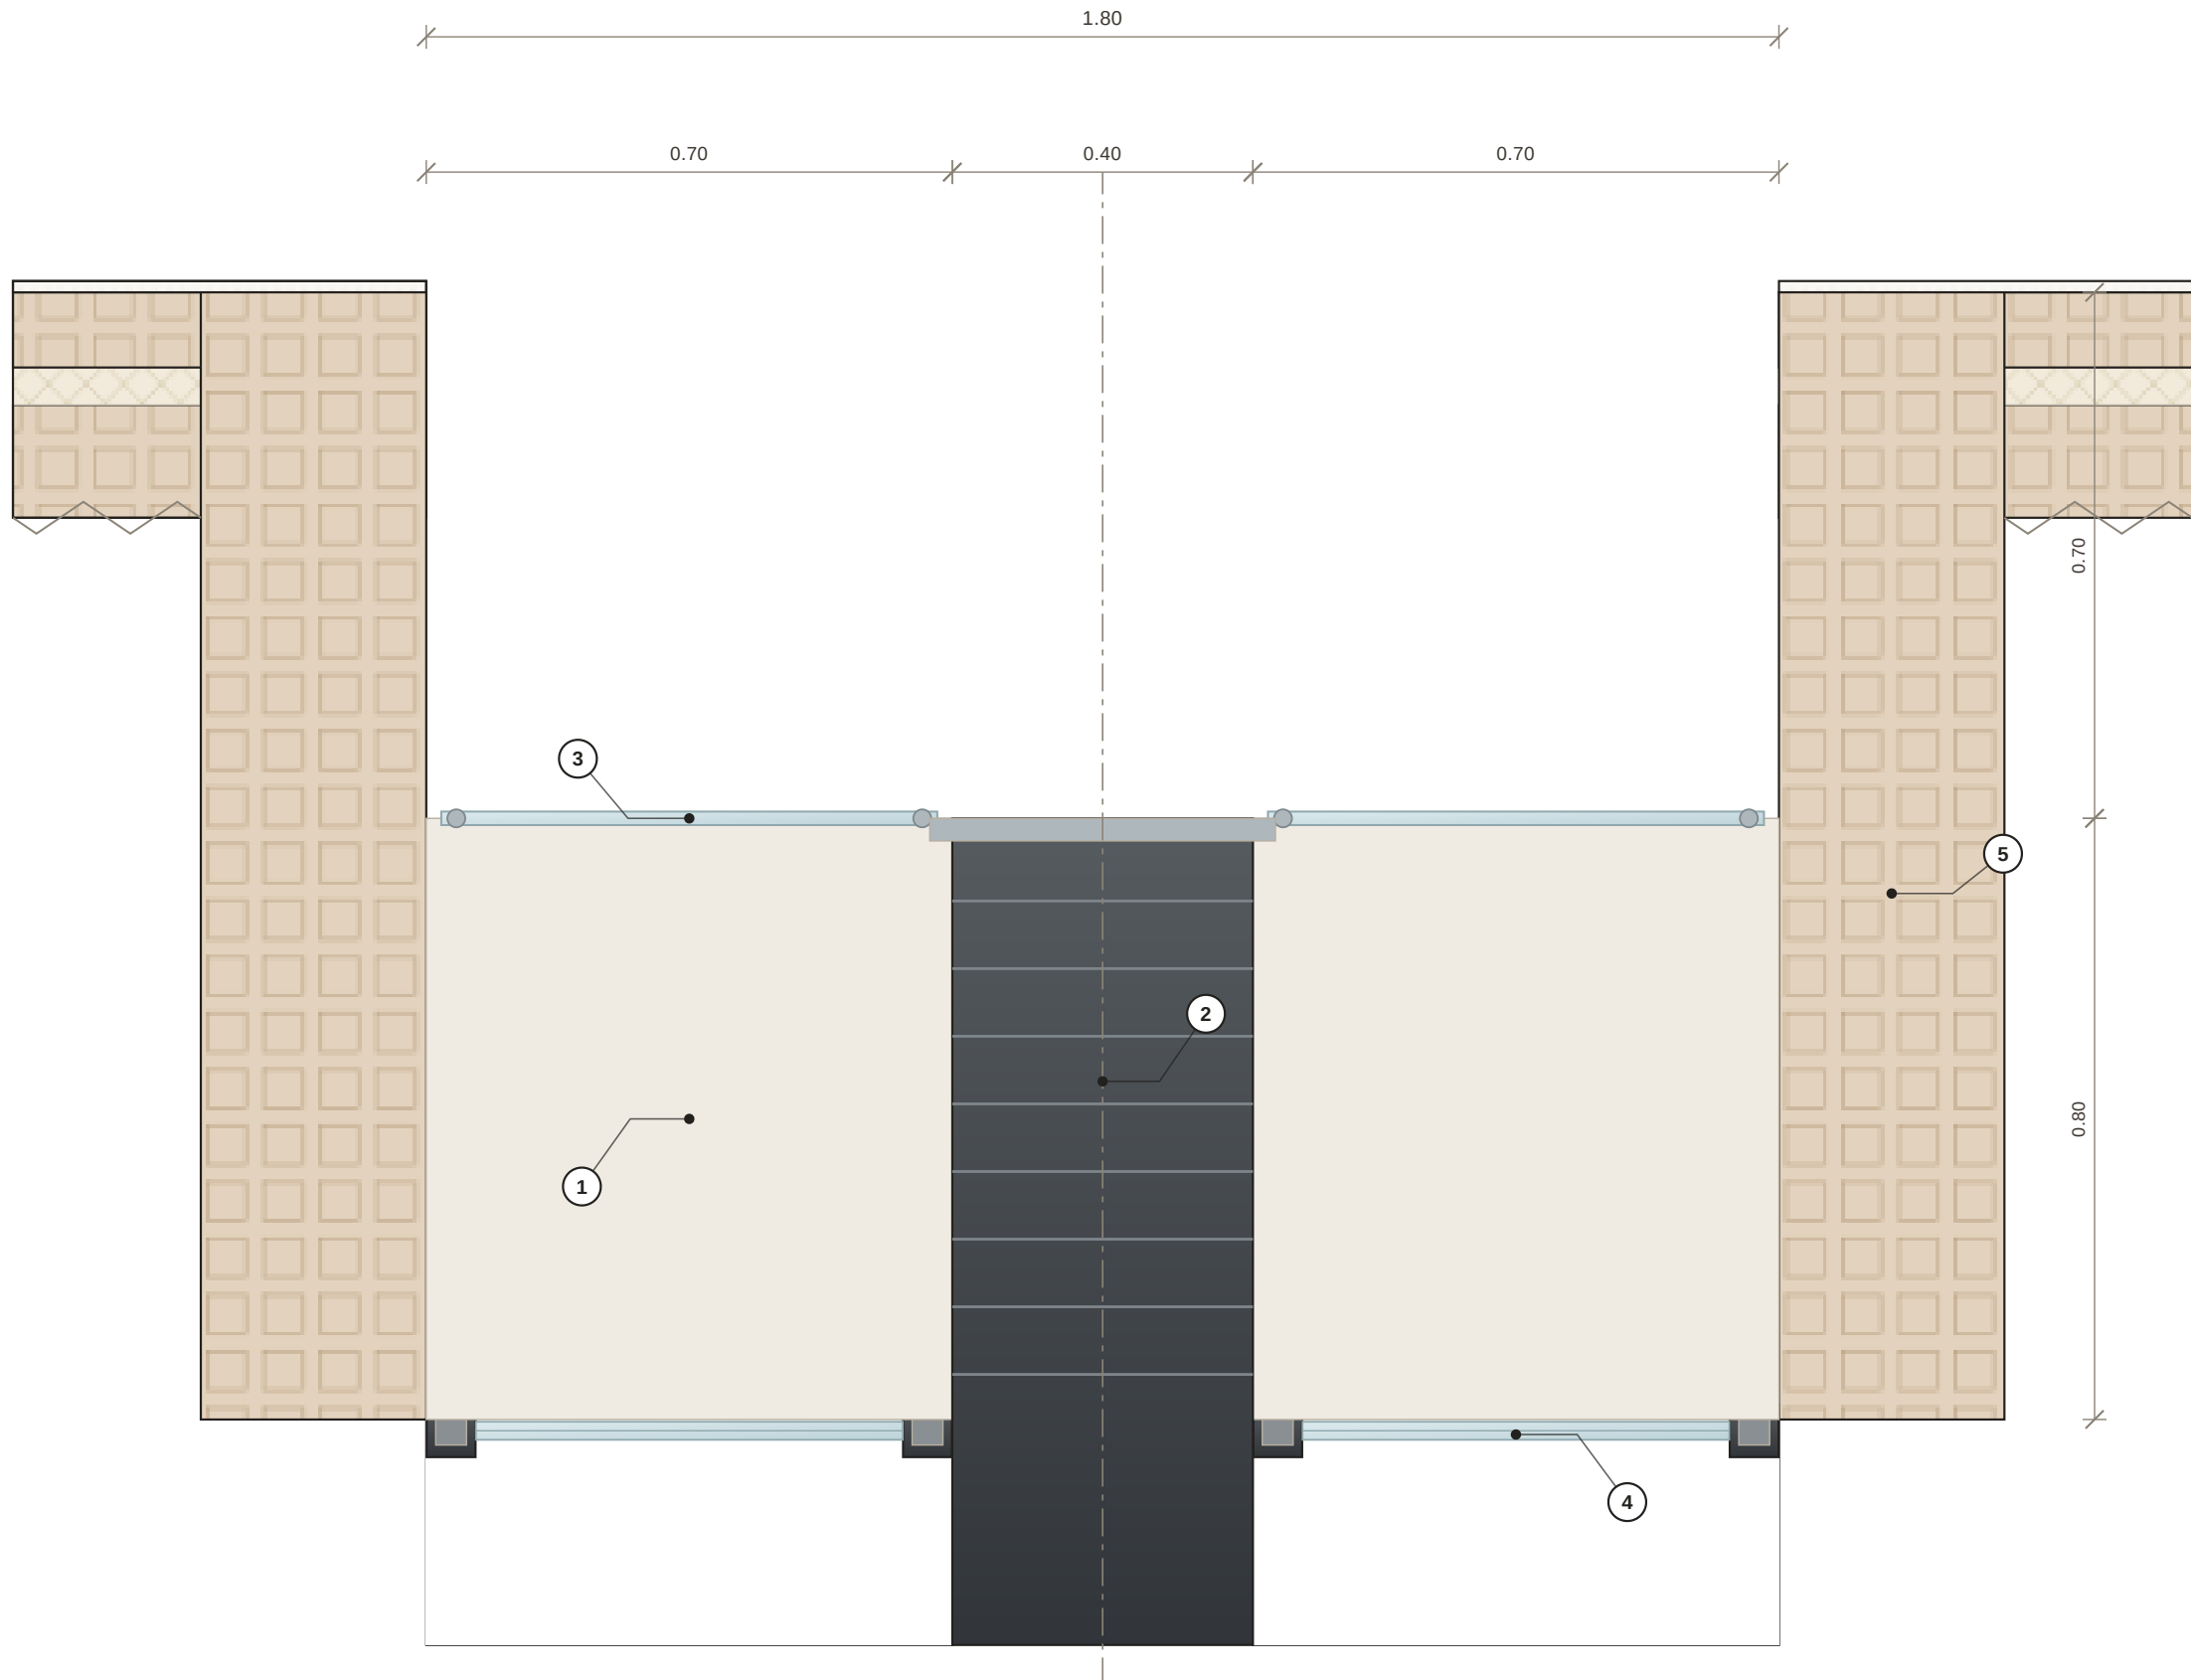


NOMENCLATURE

- ① Balcon du logement de gauche — 0,70 × 0,80 m
- ② Brise-vue aluminium RAL 7024, 40 cm de large, lames horizontales sur ossature alu, du refend de fond jusqu'au garde-corps
- ③ Garde-corps verre feuilleté 8.8.4, h 1,10 m, 2 pinces inox par panneau — il s'arrête à 0,70 m en arrière du nu : la fente reste ouverte devant
- ④ Porte-fenêtre 0,70 m depuis le logement, alu TPR 65 RAL 7024
- ⑤ Flanc de la fente : brique + monocouche, retour de 1,50 m

H2 · TRUMEAU ENTRE LES DEUX PORTES-BALCON

ÉCHELLE 1:10 · COUPE HORIZONTALE À +1,50

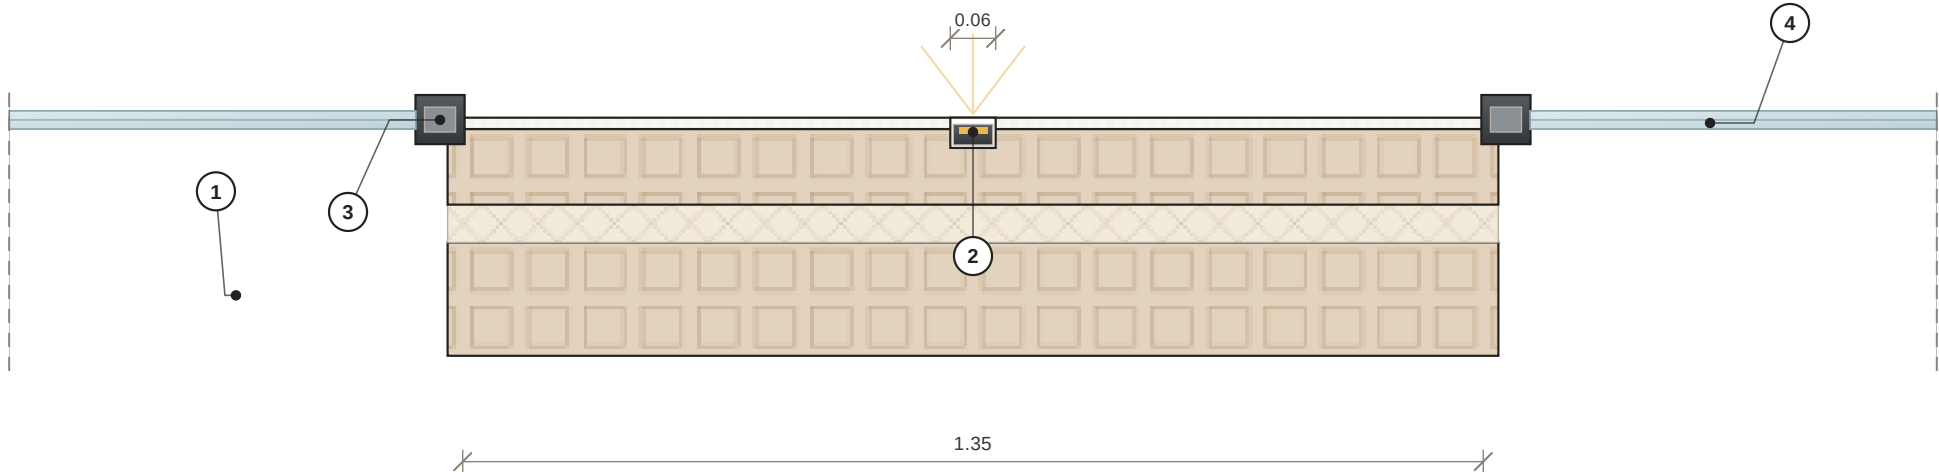

NOMENCLATURE

- ① Trumeau de 1,35 m entre les deux porte-balcon d'un même balcon
- ② Profil LED vertical encastré 60 × 40 mm, hauteur 1,90 m, 3000 K, diffuseur affleurant le monocouche — même circuit que la gorge de rive
- ③ Montants alu TPR 65 des deux baies, RAL 7024
- ④ Double vitrage 4/16/4 — porte-balcon 1,80 × 2,20 m