


Le garde-corps, panneau par panneau

Le garde-corps suit la rive par une suite de cordes de 40 cm : un panneau de verre feuilleté plat, puis 40 cm de barreaudage inox, en alternance sur les 9.63 ml développés — 24 panneaux par balcon. Le barreaudage épouse n'importe quel rayon ; le verre, plat, s'écarte de la courbe de 5 à 10 mm sur la plus grande partie de la rive et de 23 mm au plus défavorable. Voir G3.


G0 · GARDE-CORPS MIXTE — ÉLÉVATION DÉVELOPPÉE D'UN BALCON

ÉCHELLE 1:20 · DÉVELOPPÉ MIS À PLAT
VERRE INOX VERRE INOX

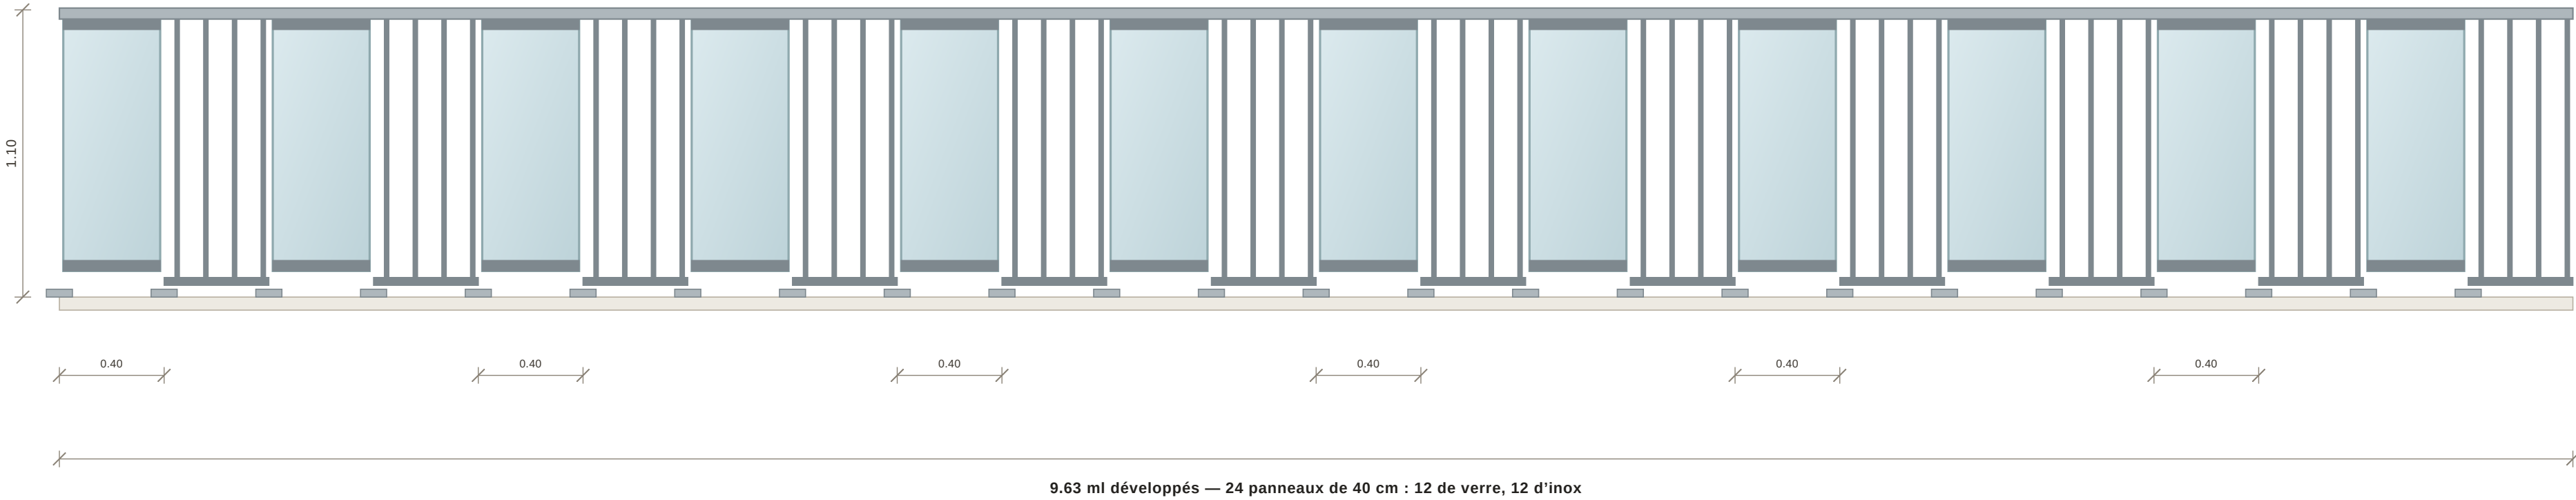

G1 · PANNEAU DE VERRE — COUPE VERTICALE

ÉCHELLE 1:5

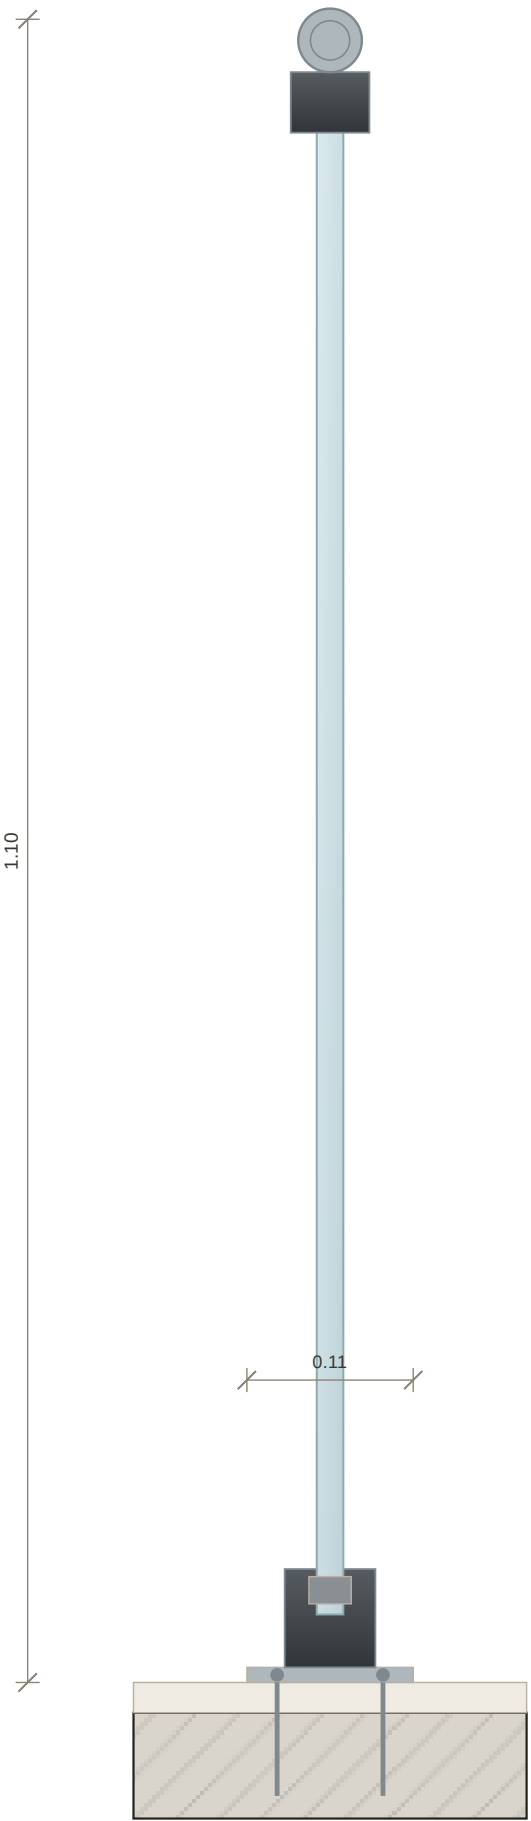


NOMENCLATURE

- Verre feuilleté 8.8.4 (17.5 mm), panneau plat de 40 cm
- Pincés inox 316 haute et basse, cale EPDM, serrage à la clé dynamo.
- Platine inox 110 × 110 × 10, 2 goujons M10 inox scellés dans la dalle
- Main courante inox Ø 42 × 2 mm, brossée grain 240, continue

G2 · BARREAUDAGE INOX — COUPE VERTICALE

ÉCHELLE 1:5

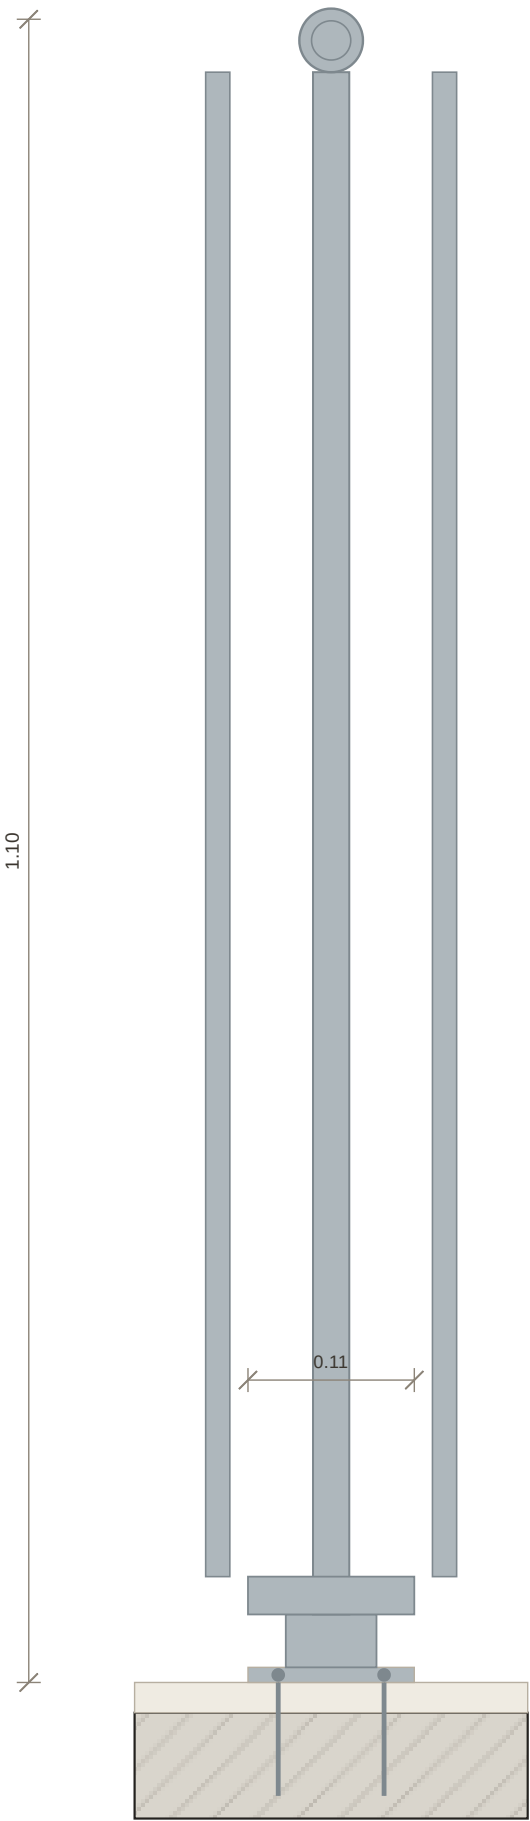


NOMENCLATURE

- Barreaux inox 316 Ø 16, entraxe 11 cm — moins de 11 cm entre nus
- Lisse basse inox 110 × 25, soudée sur les montants
- Montants inox Ø 42 aux deux extrémités de chaque section de 40 cm
- Même platine et même main courante que le panneau de verre

G3 · CE QUE COÛTE UNE CORDE DE 40 cm

AGRANDISSEMENT · PANNEAU LE PLUS DÉFAVORABLE, AU CREUX MÉDIAN

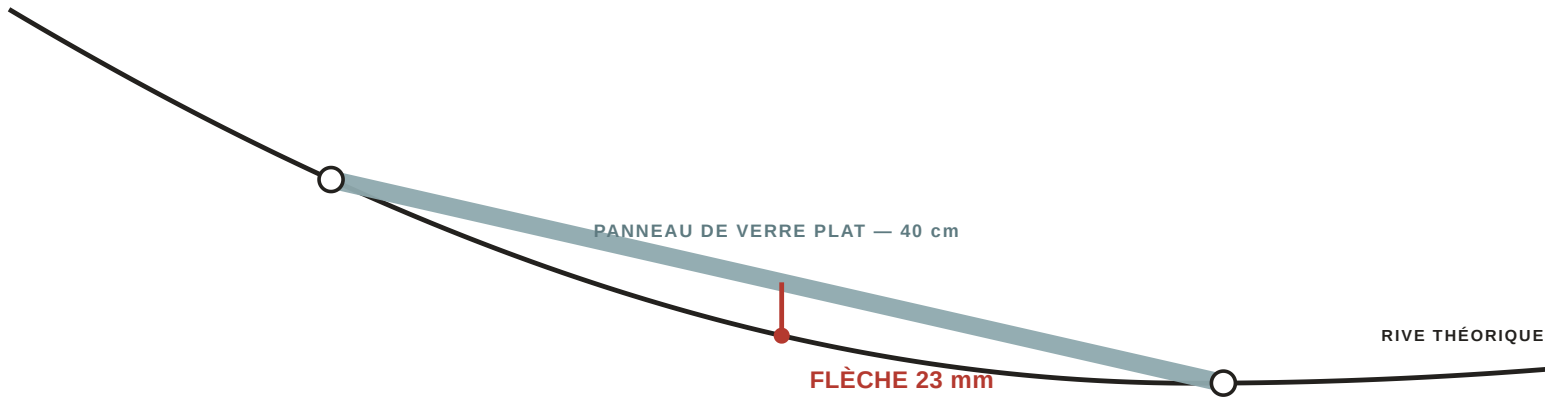

NOMENCLATURE

Un panneau plat de 40 cm posé sur la rive s'écarte au maximum de 23 mm de la courbe théorique — et seulement dans les deux zones les plus serrées (rayon 0.77 m à la crête et au creux). Ailleurs c'est 5 à 10 mm.

Rotation d'un panneau de verre au suivant : 27° au plus défavorable. Elle demande des pincés à rotule, pas des pincés droites — à vérifier avec le fournisseur avant commande.

SI VOUS VOULEZ LA COURBE PLUS FRANCHE : passer les panneaux à 20 cm dans les deux zones serrées ramène la flèche à 6 mm et la rotation à 9°. Le rythme 40/40 reste lisible partout ailleurs.